


PRINCIPAL DIMENSIONS

DIMENSION	VALUE (IN)	TAG
INTERIOR CLEAR HEIGHT	80.0	FIXED
OVERALL LENGTH / LOWER LENGTH	121.0 / 97.0	FIXED
BODY WIDTH	80.0	PARAMETRIC
TUB WIDTH / TUB BASE WIDTH	59.5 / 49.4	VERIFY ON TRUCK
INTERIOR FLOOR WIDTH (TUB BASE)	45.9	VERIFY ON TRUCK
INTERIOR WIDTH ABOVE RAILS	76.5	PRELIMINARY
NOSE INTERIOR HEIGHT / PROJECTION	35.0 / 24.0	VERIFY ON TRUCK
GROUND TO CROWN ON 2011 F-350 4X4	126.75 (10 FT 6.75 IN)	VERIFY ON TRUCK

DIMENSION TAGS (FULL LIST: DIMENSIONS.MD)

TAG	MEANING
FIXED	OWNER REQUIREMENT; CHANGE ONLY BY DECISION RECORD
PARAMETRIC	DESIGN VARIABLE IN DIMENSIONS.JSON
PRELIMINARY	PLACEHOLDER, EXPECTED TO CHANGE (V0.2/V0.3)
VERIFY ON TRUCK	DEPENDS ON THE PHYSICAL TRUCK, FLAG NOTE 1

REVISIONS			
REV	DESCRIPTION	DATE	APPROVED
A	V0.1 ENVELOPE - INITIAL RELEASE FOR OWNER REVIEW	2026-10-01	-
B	97 IN FULL-LENGTH (ADR 0004), 2011 F-350 DATA, TUB 59.5, ASME Y14 FORMAT, ADD A03-A05	2026-10-01	-

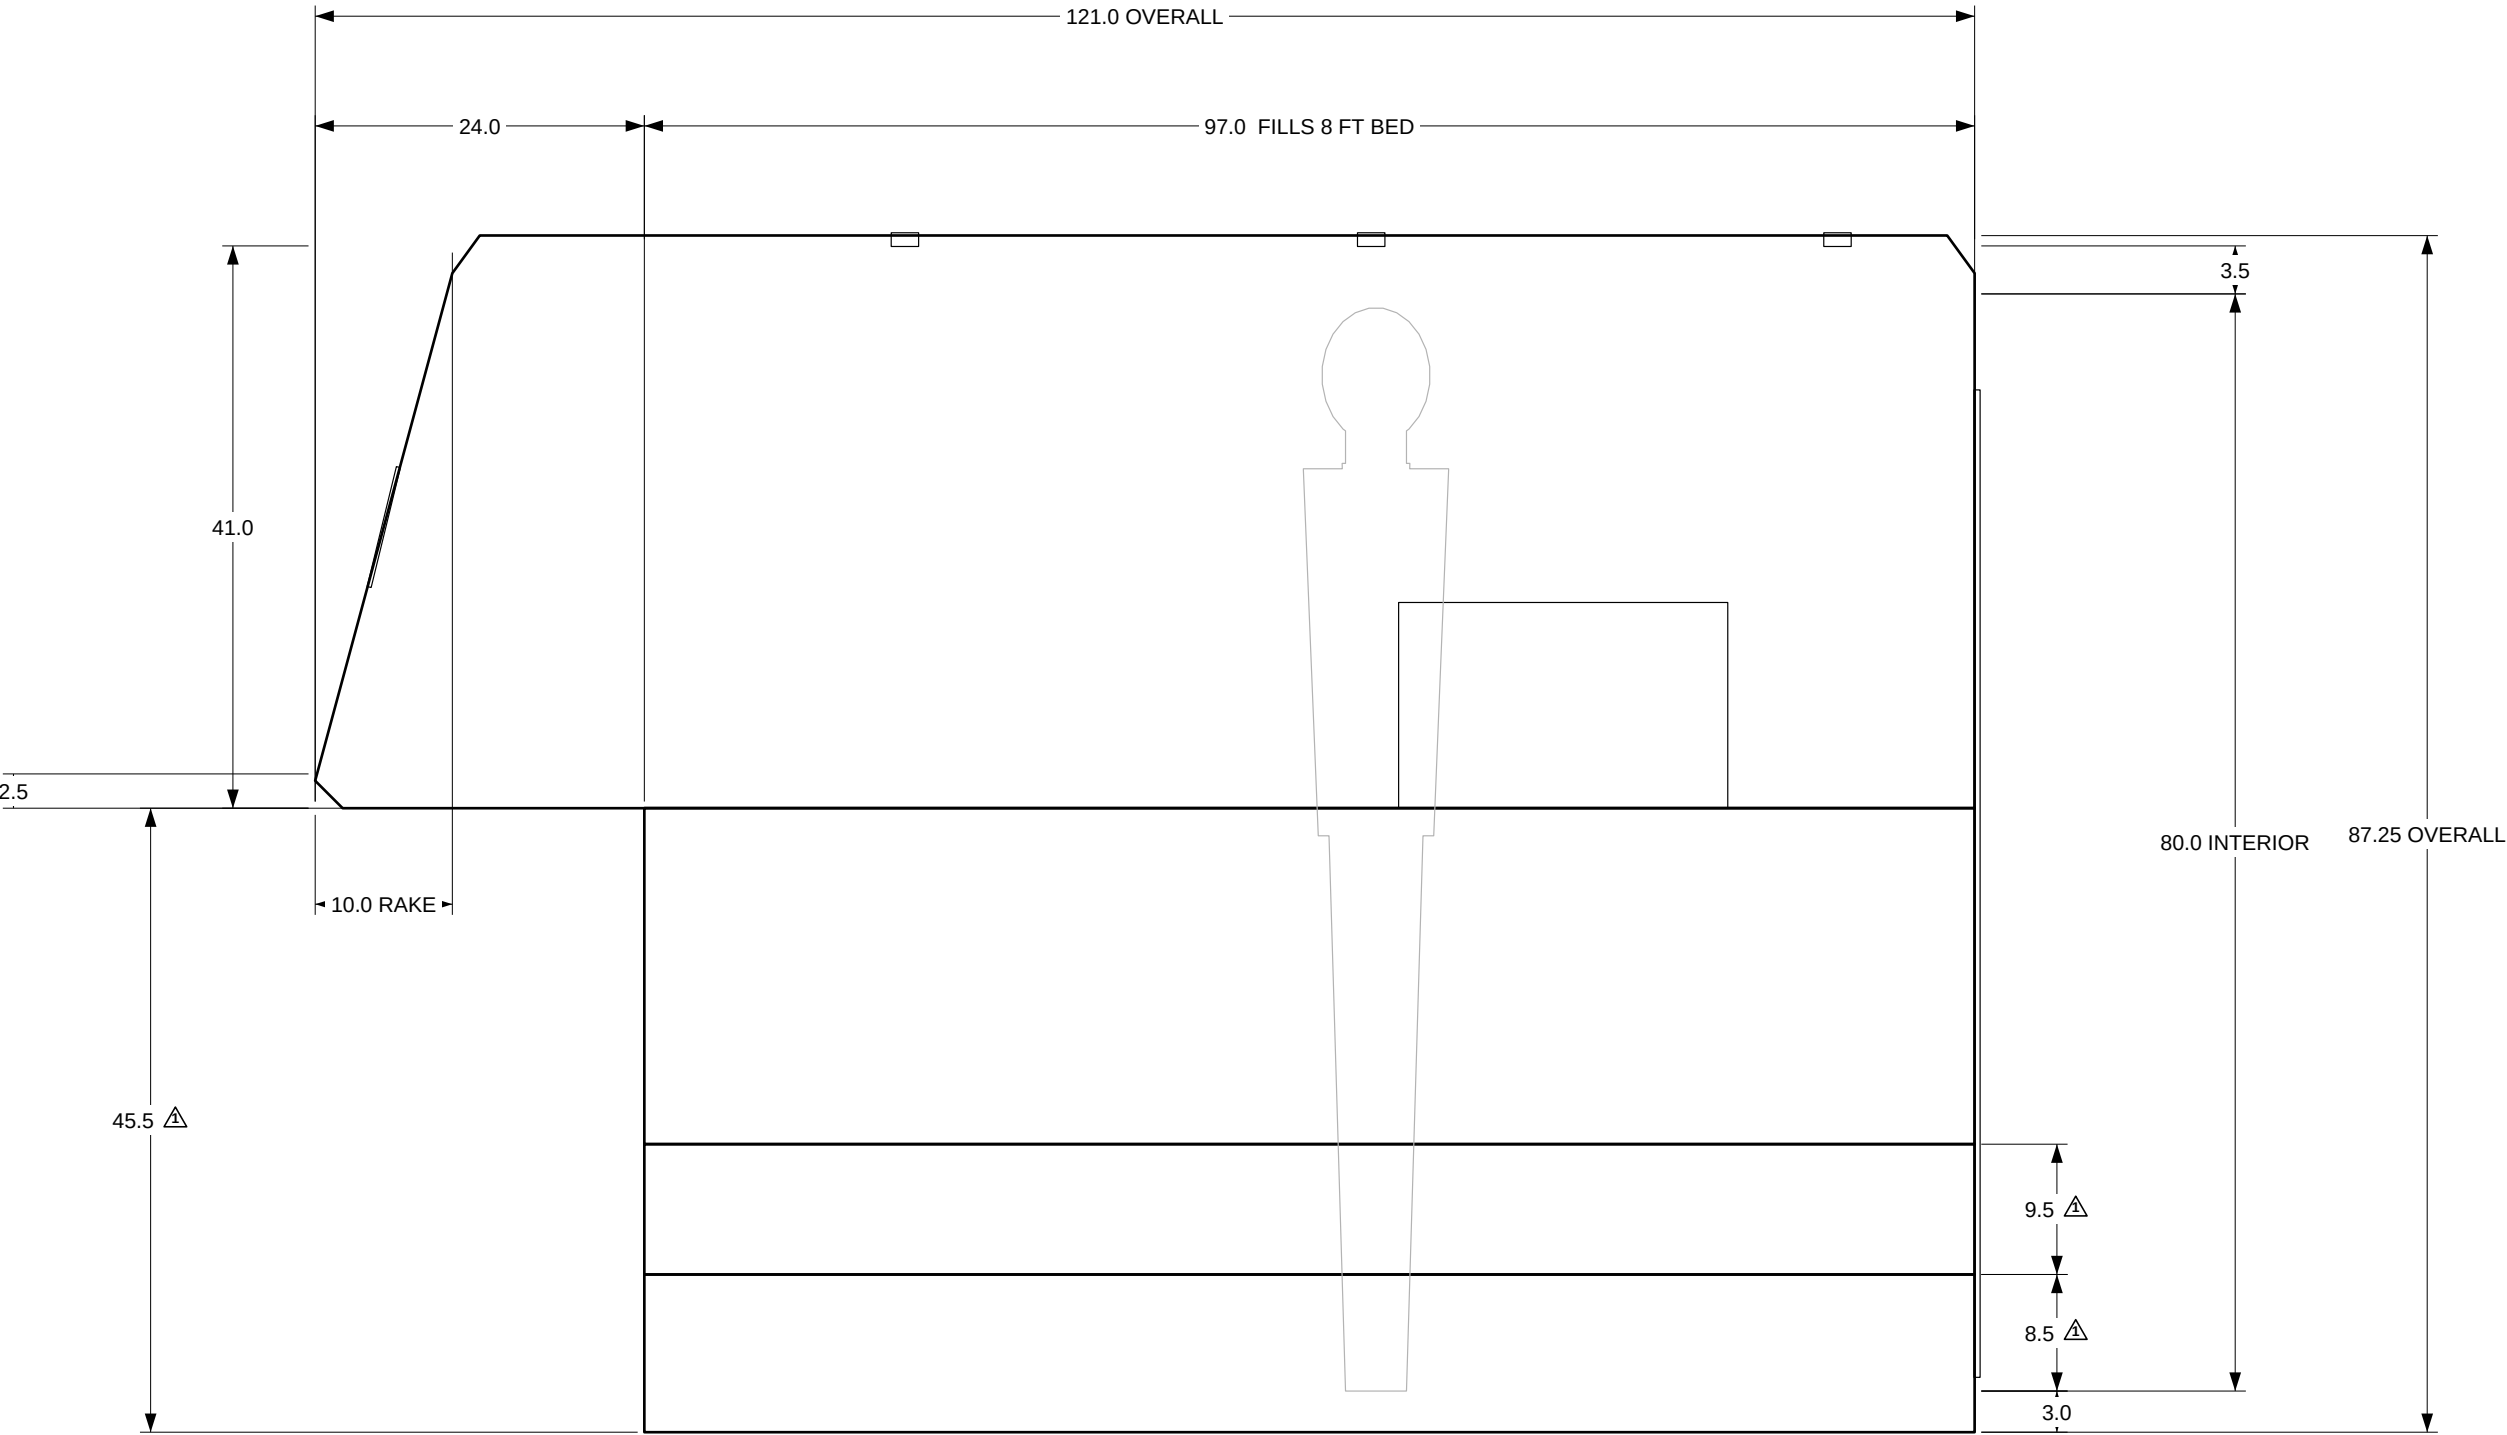


LEFT ELEVATION

SCALE 1:14 FRONT TO LEFT 6'7" FIGURE FOR SCALE

NOTES:

- VERIFY ON TRUCK: VALUE DEPENDS ON THE PHYSICAL TRUCK. CONFIRM WITH TRUCK_DATA/MEASUREMENT_TEMPLATES/F350_MEASUREMENT_SHEET.PDF.
- ORIGIN: BED-FLOOR TOP, TRUCK CENTERLINE, INNER FACE OF BED FRONT WALL. CAMPER FRONT FACE .5 AFT; REAR FACE .5 AHEAD OF CLOSED TAILGATE (8 FT BED).
- INTERIOR HEIGHT 80.0 IS AN OWNER REQUIREMENT (6'7" STANDING, ADR 0002). HEADROOM OVER FIGURE 1.0.

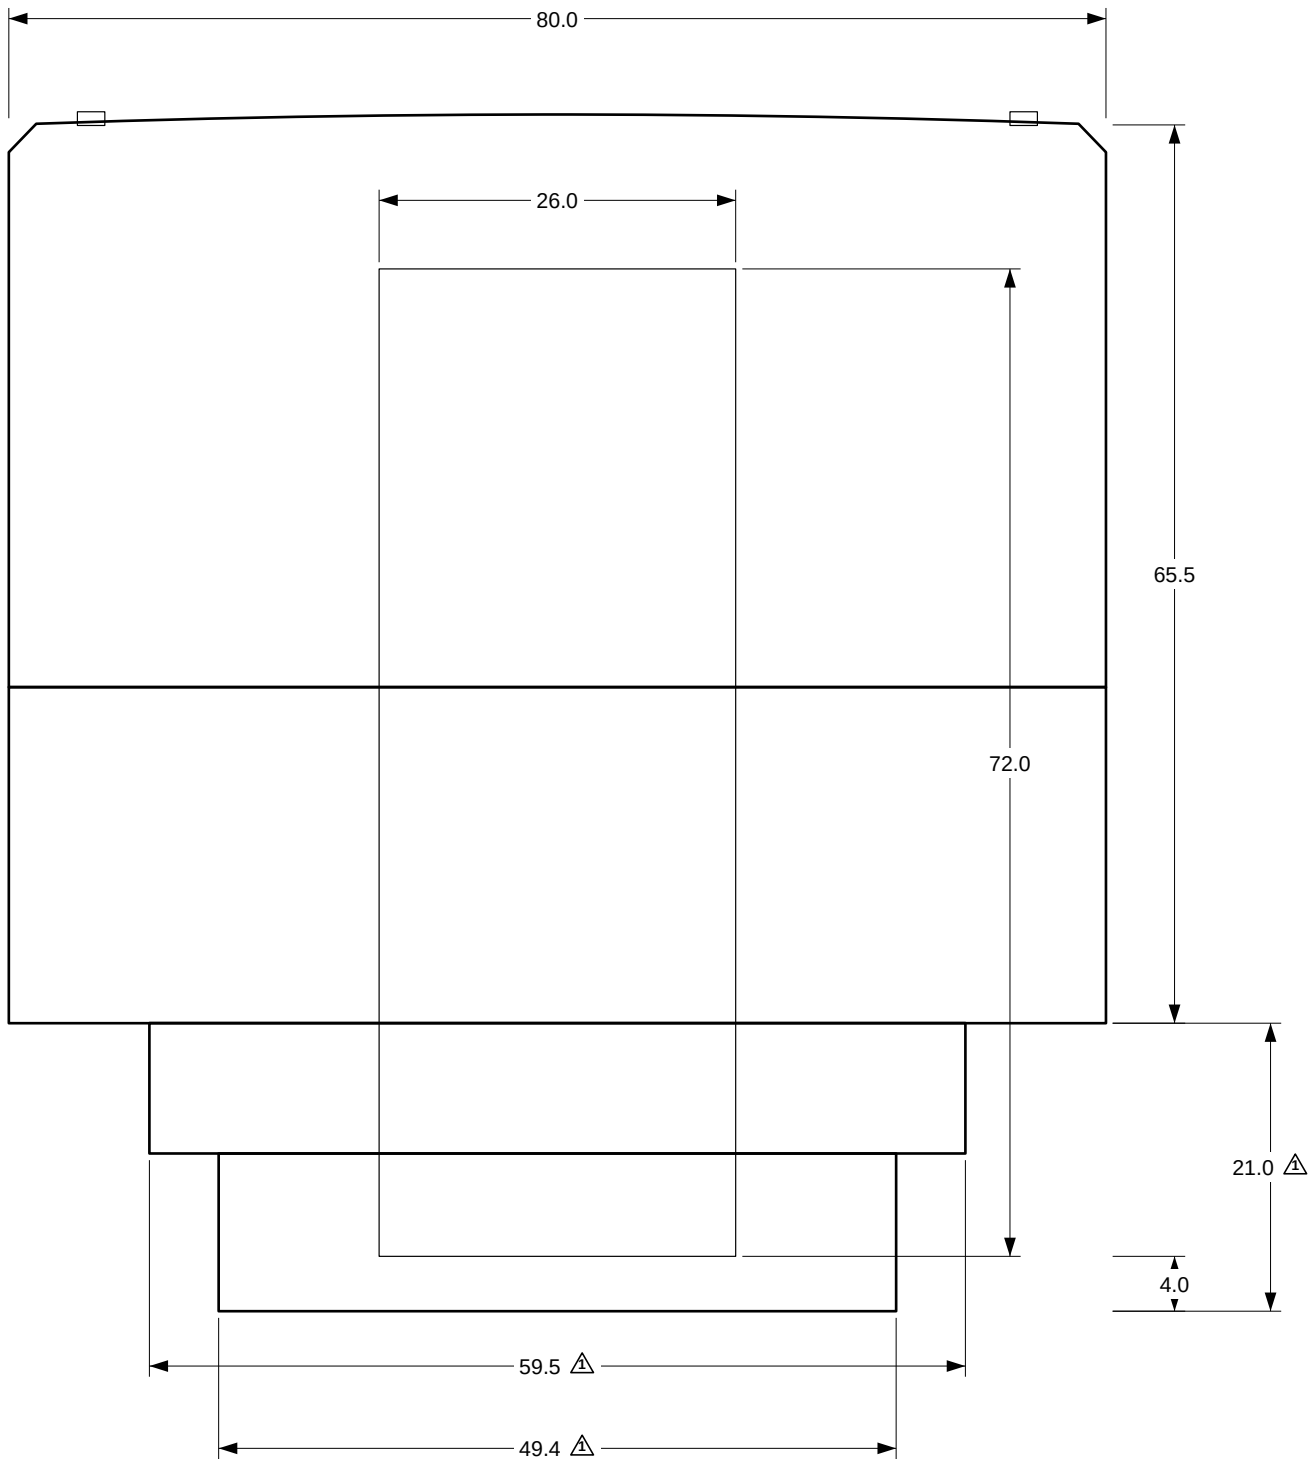

REAR ELEVATION

SCALE 1:14

UNLESS OTHERWISE SPECIFIED: DIMENSIONS ARE IN INCHES ENVELOPE = OUTSIDE OF SKIN, NOMINAL TOLERANCES: X.X +/- .25 X.XX +/- .06 ANGLES +/- 1 DEG INTERPRET PER ASME Y14.5-2018 DO NOT SCALE DRAWING THIRD ANGLE PROJECTION	PROJECT / OWNER		
	MINUTEMAN ALUMINUM SLIDE-IN CAMPER SHELL - S. ORLIK		
	TITLE		
	MAJOR DIMENSIONS		
SIZE	DWG NO.		REV
C	MM-A02		B
SCALE	DATE		SHEET
1:14	2026-10-01		2 OF 5
DRAWN	CHECKED	STATUS	
CLAUDE (A) FOR S.O.	-	PRELIMINARY - NOT FOR FABRICATION	