
REVISIONS			
REV	DESCRIPTION	DATE	APPROVED
A	V0.1 ENVELOPE - INITIAL RELEASE FOR OWNER REVIEW	2026-10-01	-
B	97 IN FULL-LENGTH (ADR 0004), 2011 F-350 DATA, TUB 59.5, ASME Y14 FORMAT, ADD A03-A05	2026-10-01	-

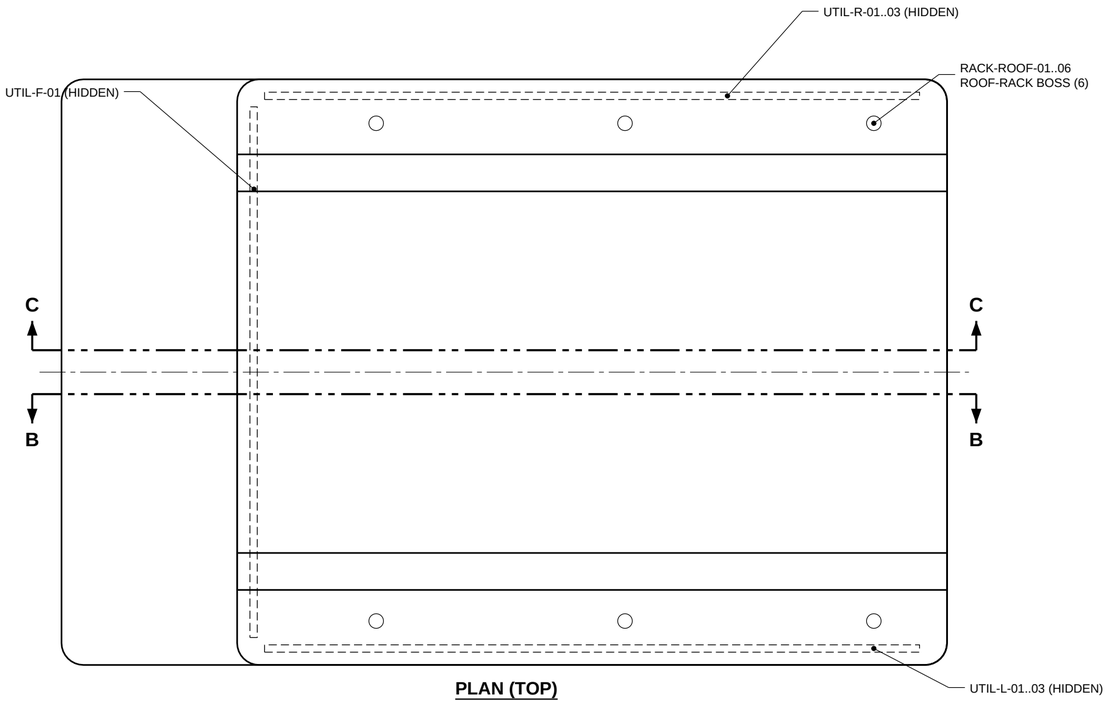


PLAN (TOP)
SCALE 1:16 FRONT TO LEFT

PARTS LIST (FROM CAD REGISTRY)


ITEM	PART ID	DESCRIPTION
1	ENV-TUB-01	LOWER TUB ENVELOPE
2	ENV-BODY-01	MAIN BODY ENVELOPE
3	ENV-NOSE-01	NOSE ENVELOPE
4	ENV-ROOF-01	ROOF ENVELOPE
5	DOOR-B-01	REAR ENTRY DOOR PLACEHOLDER
6	WIN-L-01	SIDE WINDOW PLACEHOLDER
7	WIN-R-01	SIDE WINDOW PLACEHOLDER
8	WIN-N-01	NOSE WINDOW PLACEHOLDER (OPTIONAL)
9	RACK-ROOF-01	ROOF-RACK MOUNTING BOSS
10	RACK-ROOF-02	ROOF-RACK MOUNTING BOSS
11	RACK-ROOF-03	ROOF-RACK MOUNTING BOSS
12	RACK-ROOF-04	ROOF-RACK MOUNTING BOSS
13	RACK-ROOF-05	ROOF-RACK MOUNTING BOSS
14	RACK-ROOF-06	ROOF-RACK MOUNTING BOSS
15	UTIL-L-01	OWNER ACCESSORY T-SLOT RAIL
16	UTIL-L-02	OWNER ACCESSORY T-SLOT RAIL
17	UTIL-L-03	OWNER ACCESSORY T-SLOT RAIL
18	UTIL-R-01	OWNER ACCESSORY T-SLOT RAIL
19	UTIL-R-02	OWNER ACCESSORY T-SLOT RAIL
20	UTIL-R-03	OWNER ACCESSORY T-SLOT RAIL
21	UTIL-F-01	OWNER ACCESSORY T-SLOT RAIL

NOTES:


1. V0.1 IS AN ENVELOPE ONLY: OUTER SKIN SURFACES. NO STRUCTURAL FRAME IS SHOWN OR IMPLIED.
2. PART IDS FOLLOW SYSTEM-LOCATION-NUMBER (CAD/CONFIG/PART_IDS.MD) AND MATCH BOM, RENDERS AND MANUAL.
3. HIDDEN LINES: OWNER ACCESSORY T-SLOT RAILS ON INTERIOR WALL FACES. NOT PRIMARY STRUCTURE.
4. RACK-ROOF BOSSES ARE STRUCTURAL PROVISIONS; EACH MUST LAND ON A ROOF CROSSMEMBER (V0.2).
5. DOOR AND WINDOWS ARE ROUGH-OPENING PLACEHOLDERS FOR PURCHASED COMPONENTS. WIN-R-01 MIRRORS WIN-L-01.
6. NOSE IS STORAGE / DESK VOLUME ONLY; NOT ENGINEERED AS A SLEEPING PLATFORM.
7. DIMENSIONS: SEE MM-A02. INTERIOR SECTIONS B-B, C-C: MM-A03. TRUCK FIT: MM-A04, MM-A05.
⚠1 VERIFY ON TRUCK: VALUE DEPENDS ON THE PHYSICAL TRUCK. CONFIRM WITH TRUCK_DATA/MEASUREMENT_TEMPLATES/F350_MEASUREMENT_SHEET.PDF.

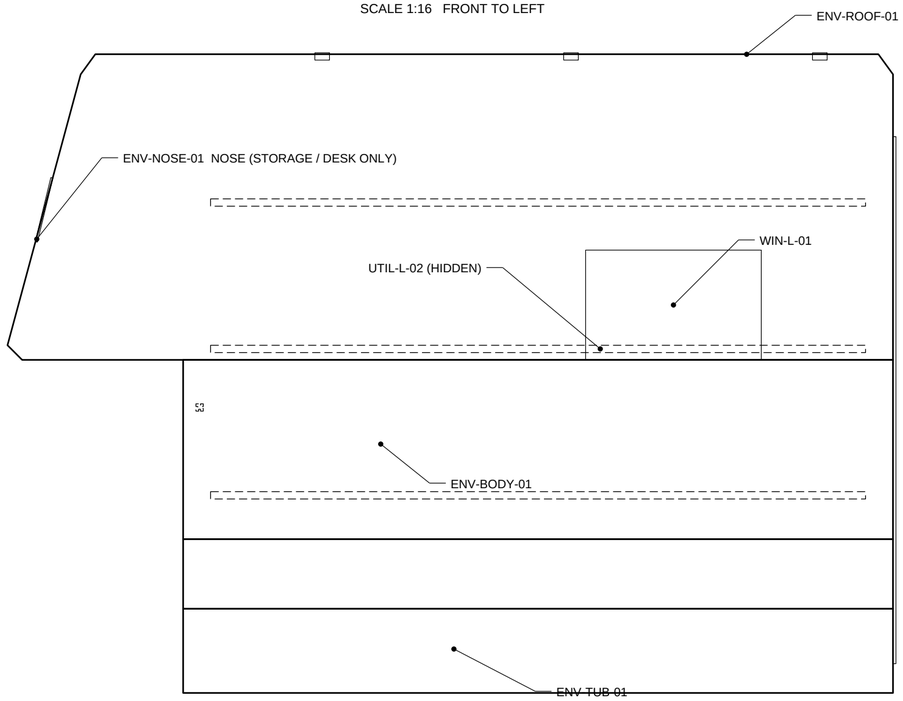

LEFT ELEVATION
SCALE 1:16 FRONT TO LEFT

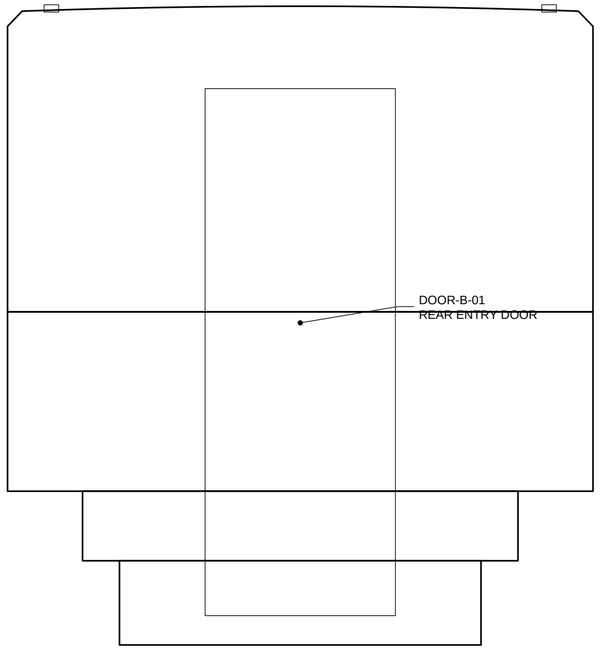

REAR ELEVATION
SCALE 1:16

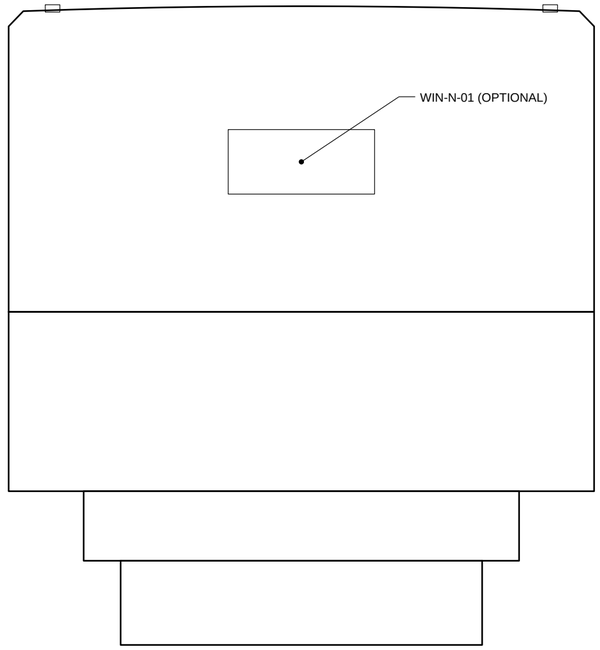

FRONT ELEVATION
SCALE 1:16

UNLESS OTHERWISE SPECIFIED:
DIMENSIONS ARE IN INCHES
ENVELOPE = OUTSIDE OF SKIN, NOMINAL
TOLERANCES:
X.X +/- .25 X.XX +/- .06
ANGLES +/- 1 DEG
INTERPRET PER ASME Y14.5-2018
DO NOT SCALE DRAWING

THIRD ANGLE PROJECTION

PROJECT / OWNER
MINUTEMAN ALUMINUM SLIDE-IN CAMPER SHELL - S. ORLIK

TITLE
GENERAL ARRANGEMENT

SIZE	DWG NO.	REV
C	MM-A01	B

SCALE	DATE	SHEET
1:16	2026-10-01	1 OF 5

DRAWN	CHECKED	STATUS
CLAUDE (AI) FOR S.O.	-	**PRELIMINARY - NOT FOR FABRICATION**