

REVISIONS			
REV	DESCRIPTION	DATE	APPROVED
A	V0.1 ENVELOPE - INITIAL RELEASE FOR OWNER REVIEW	2026-10-01	-
B	97 IN FULL-LENGTH (ADR 0004), 2011 F-350 DATA, TUB 59.5, ASME Y14 FORMAT, ADD A03-A05	2026-10-01	-

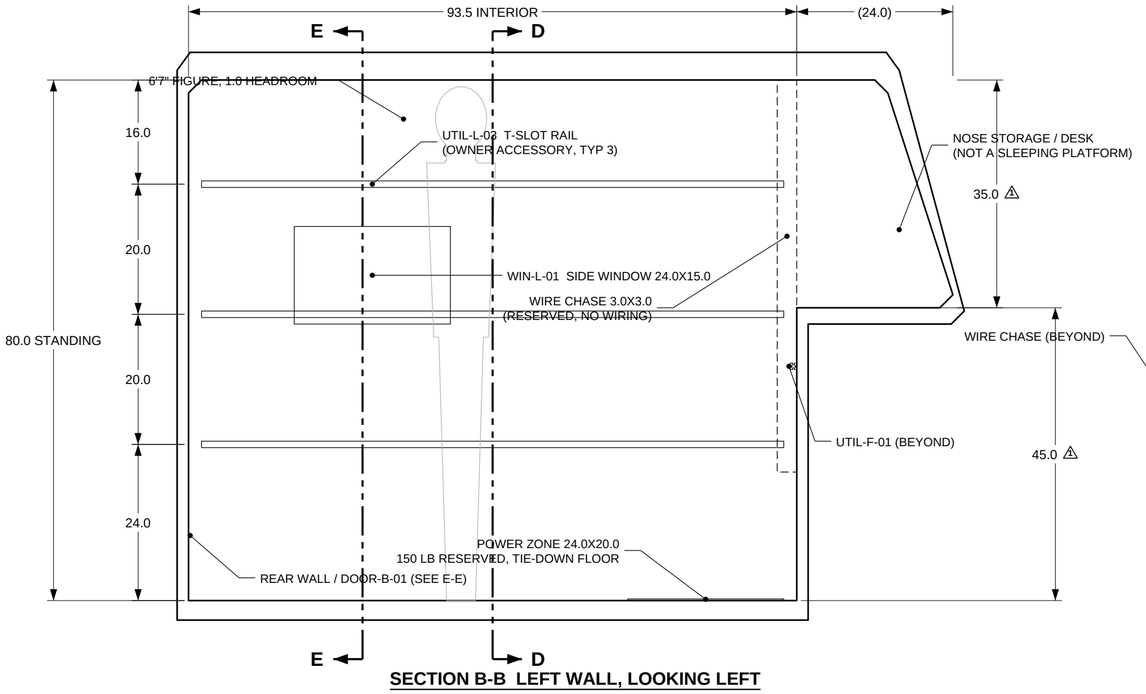


SECTION B-B LEFT WALL, LOOKING LEFT

SCALE 1:18 FRONT TO RIGHT

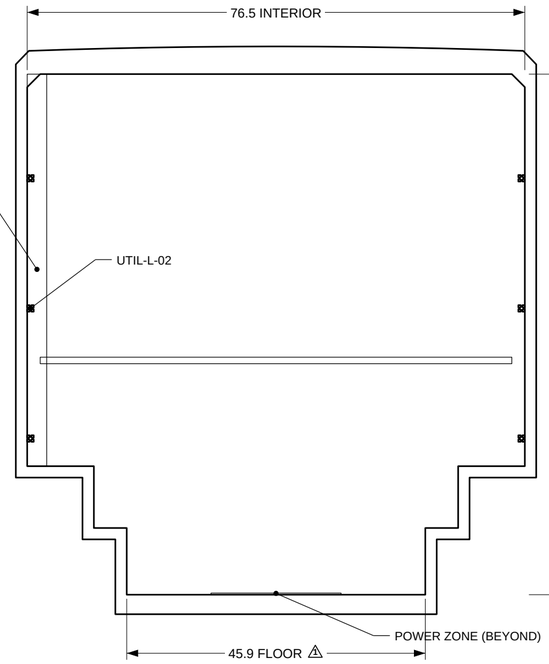


SECTION D-D LOOKING FORWARD

SCALE 1:18 AT X = -49.0

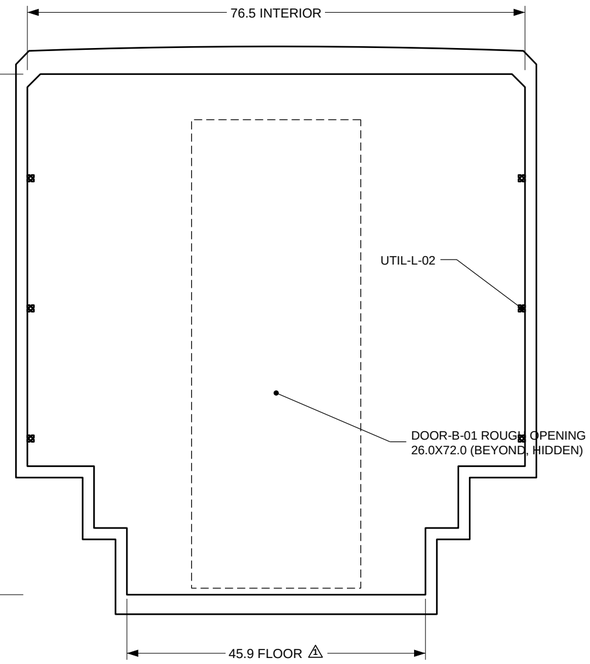

SECTION E-E LOOKING AFT

SCALE 1:18 AT X = -69.0

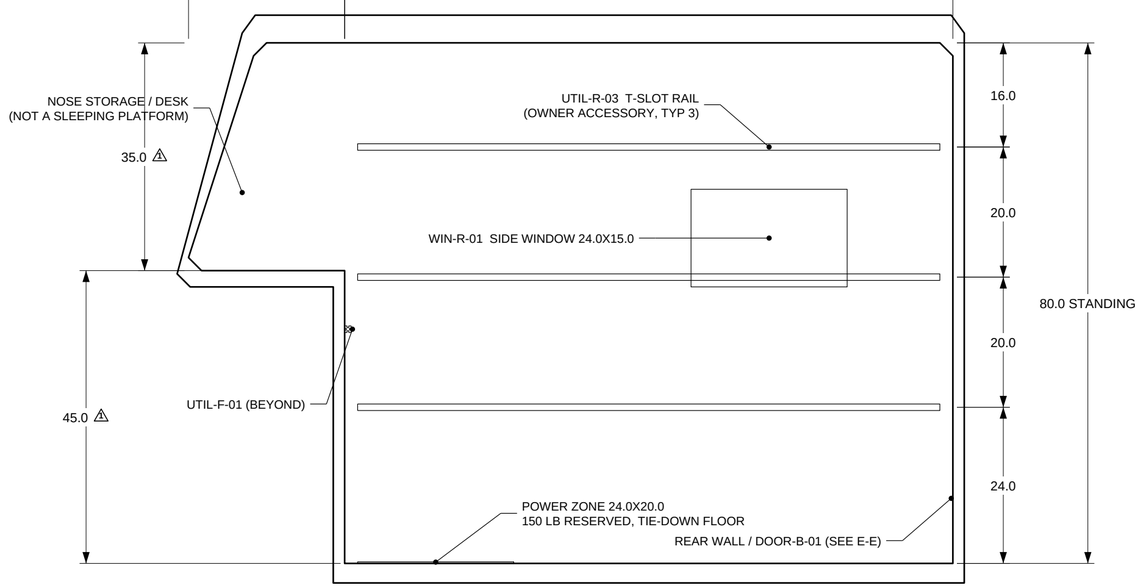

SECTION C-C RIGHT WALL, LOOKING RIGHT

SCALE 1:18 FRONT TO LEFT

NOTES:

1. SHELL ONLY. NO FURNITURE, BED, KITCHEN, WATER OR ELECTRICAL SYSTEMS ARE PART OF THIS DESIGN; THE INTERIOR IS LEFT OPEN FOR THE OWNER.
2. SECTIONS SHOW THE INTERIOR SURFACE ENVELOPE AT PRELIMINARY WALL 1.75, FLOOR 3.0, ROOF 3.5 THICKNESS.
3. T-SLOT RAIL HEIGHTS ABOVE FLOOR: 24.0, 44.0, 64.0. RAILS BOLT INTO FRAME MEMBERS (V0.2), NEVER SKIN ONLY.
4. POWER ZONE AND WIRE CHASE ARE RESERVED GEOMETRY (ADR 0003): STRUCTURE ONLY, NO ELECTRICAL DESIGN.

⚠1 VERIFY ON TRUCK: VALUE DEPENDS ON THE PHYSICAL TRUCK. CONFIRM WITH TRUCK_DATA/MEASUREMENT_TEMPLATES/F350_MEASUREMENT_SHEET.PDF.

UNLESS OTHERWISE SPECIFIED:
DIMENSIONS ARE IN INCHES
ENVELOPE = OUTSIDE OF SKIN, NOMINAL
TOLERANCES:
X.X +/- .25 X.XX +/- .06
ANGLES +/- 1 DEG
INTERPRET PER ASME Y14.5-2018
DO NOT SCALE DRAWING

THIRD ANGLE PROJECTION

PROJECT / OWNER
MINUTEMAN ALUMINUM SLIDE-IN CAMPER SHELL - S. ORLIK

TITLE
INTERIOR SECTIONS AND PROVISIONS

SIZE	DWG NO.	REV
C	MM-A03	B

SCALE	DATE	SHEET
1:18	2026-10-01	3 OF 5

DRAWN	CHECKED	STATUS
CLAUDE (AI) FOR S.O.	-	**PRELIMINARY - NOT FOR FABRICATION**