


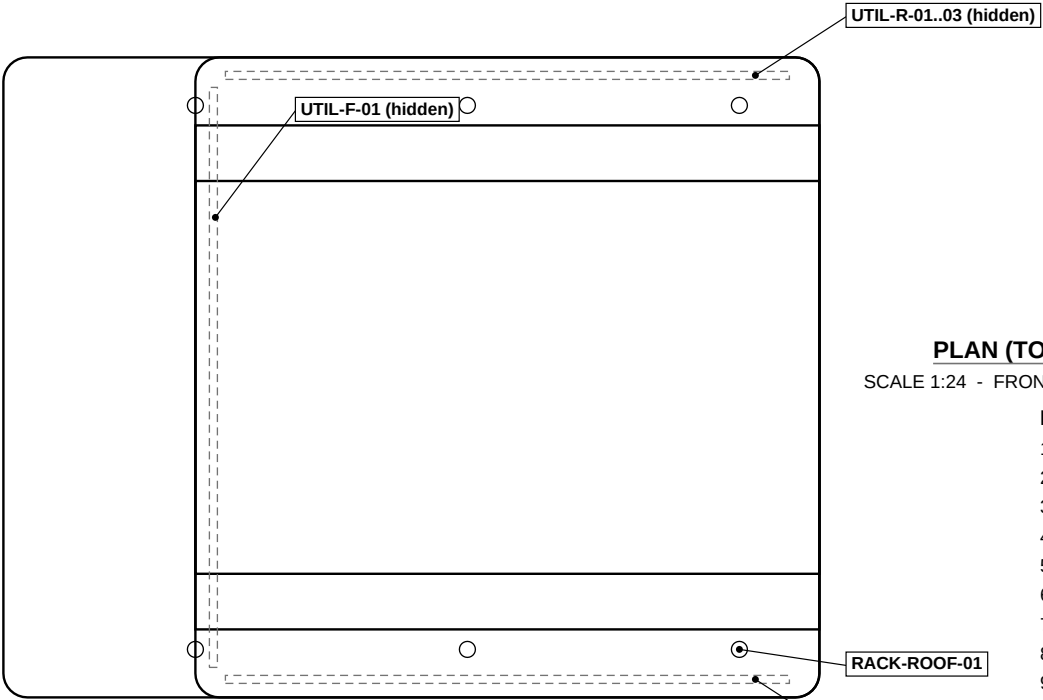


PLAN (TOP)
SCALE 1:24 - FRONT TO LEFT

NOTES


- v0.1 is an ENVELOPE ONLY: outer surfaces of the shell, no structural frame.
- All IDs follow SYSTEM-LOCATION-NUMBER (cad/config/part_ids.md) and match BOM, renders, manual.
- Hidden (dashed): owner accessory T-slot rails on interior wall faces. Not primary structure.
- RACK-ROOF bosses are structural provisions; each must land on a roof crossmember in v0.2.
- Door and windows are rough-opening placeholders for purchased components. WIN-R-01 mirrors WIN-L-01.
- Nose is storage/desk volume only; not engineered as a sleeping platform.
- Roof has 0.75" transverse drainage crown. Vertical corners R3.0".
- Dimensions: see A02. Truck fit: see A03.
- VOT = VERIFY ON TRUCK: depends on the physical truck; confirm with truck_data/measurement_templates/f350_measurement_sheet.md.

PARTS LIST (from CAD registry)


ENV-TUB-01	LOWER TUB ENVELOPE
ENV-BODY-01	MAIN BODY ENVELOPE
ENV-NOSE-01	NOSE ENVELOPE
ENV-ROOF-01	ROOF ENVELOPE
DOOR-B-01	REAR ENTRY DOOR PLACEHOLDER
WIN-L-01	SIDE WINDOW PLACEHOLDER
WIN-R-01	SIDE WINDOW PLACEHOLDER
WIN-N-01	NOSE WINDOW PLACEHOLDER (OPTIONAL)
RACK-ROOF-01	ROOF-RACK MOUNTING BOSS
RACK-ROOF-02	ROOF-RACK MOUNTING BOSS
RACK-ROOF-03	ROOF-RACK MOUNTING BOSS
RACK-ROOF-04	ROOF-RACK MOUNTING BOSS
RACK-ROOF-05	ROOF-RACK MOUNTING BOSS
RACK-ROOF-06	ROOF-RACK MOUNTING BOSS
UTIL-L-01	OWNER ACCESSORY T-SLOT RAIL
UTIL-L-02	OWNER ACCESSORY T-SLOT RAIL
UTIL-L-03	OWNER ACCESSORY T-SLOT RAIL
UTIL-R-01	OWNER ACCESSORY T-SLOT RAIL
UTIL-R-02	OWNER ACCESSORY T-SLOT RAIL
UTIL-R-03	OWNER ACCESSORY T-SLOT RAIL
UTIL-F-01	OWNER ACCESSORY T-SLOT RAIL

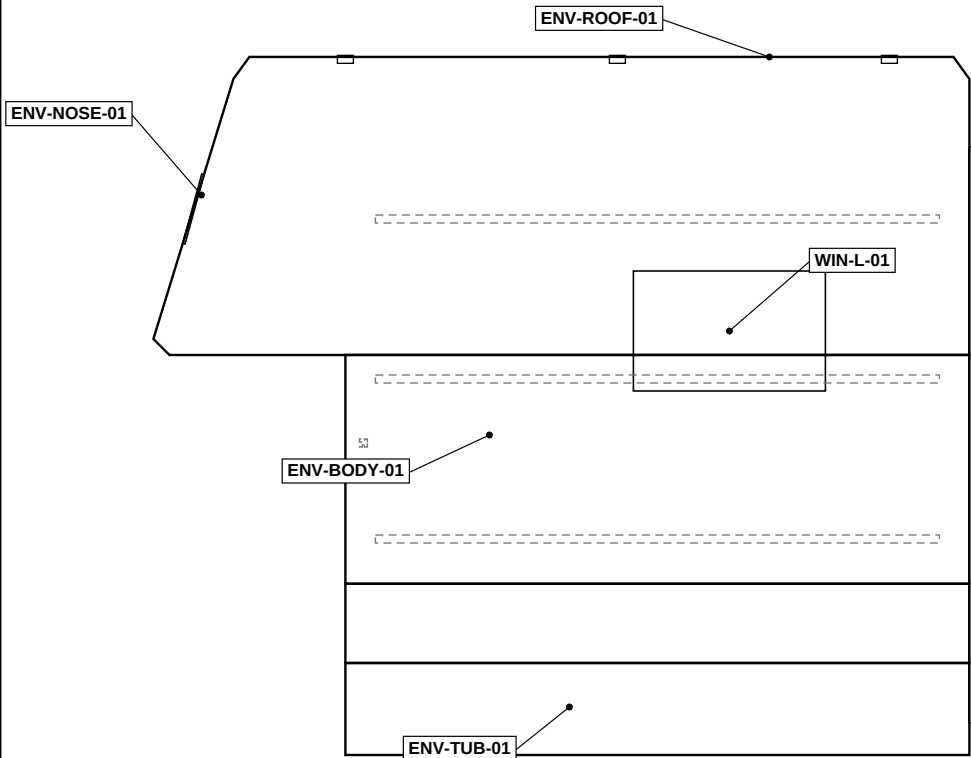

LEFT ELEVATION (DRIVER SIDE)
SCALE 1:24 - FRONT TO LEFT

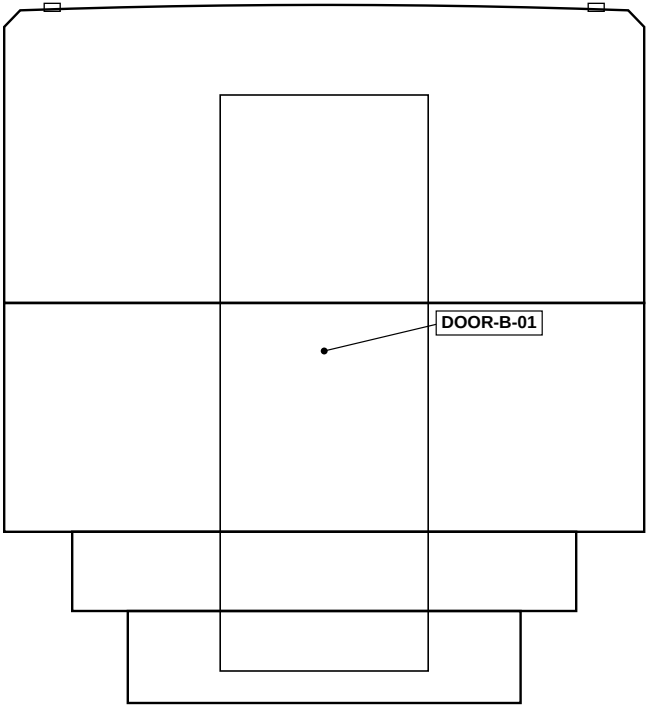

REAR ELEVATION
SCALE 1:24

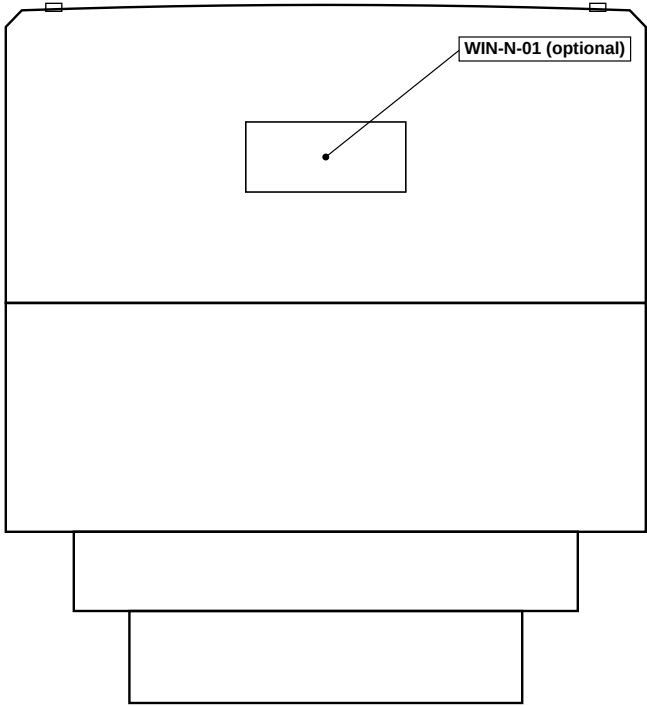

FRONT ELEVATION
SCALE 1:24

PROJECT	MINUTEMAN aluminum slide-in camper shell - v0.1 envelope
TITLE	GENERAL ARRANGEMENT
DWG NO.	A01 REV A DATE 2026-10-01
SCALE	1:24 UNITS: INCHES SHEET: ANSI B
STATUS	PRELIMINARY - CONCEPT ENVELOPE - NOT FOR FABRICATION