
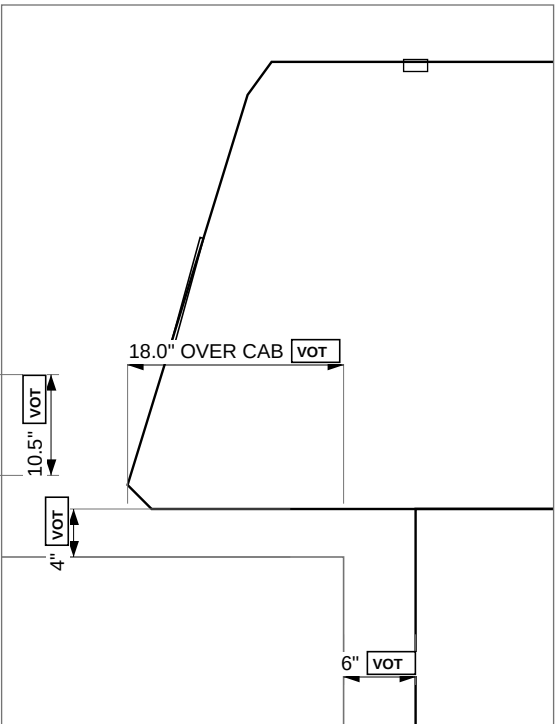
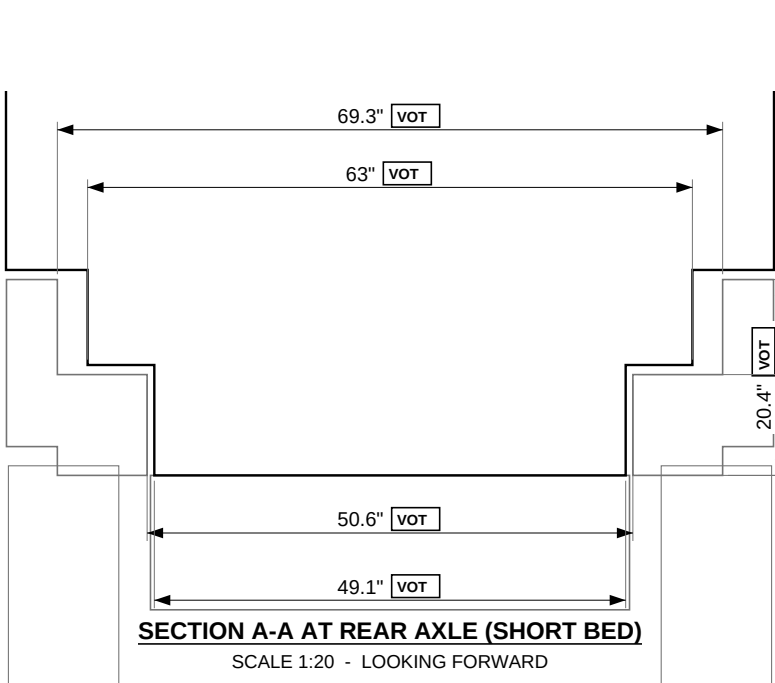



SHORT BED (6.75 FT) - LEFT ELEVATION

SCALE 1:40

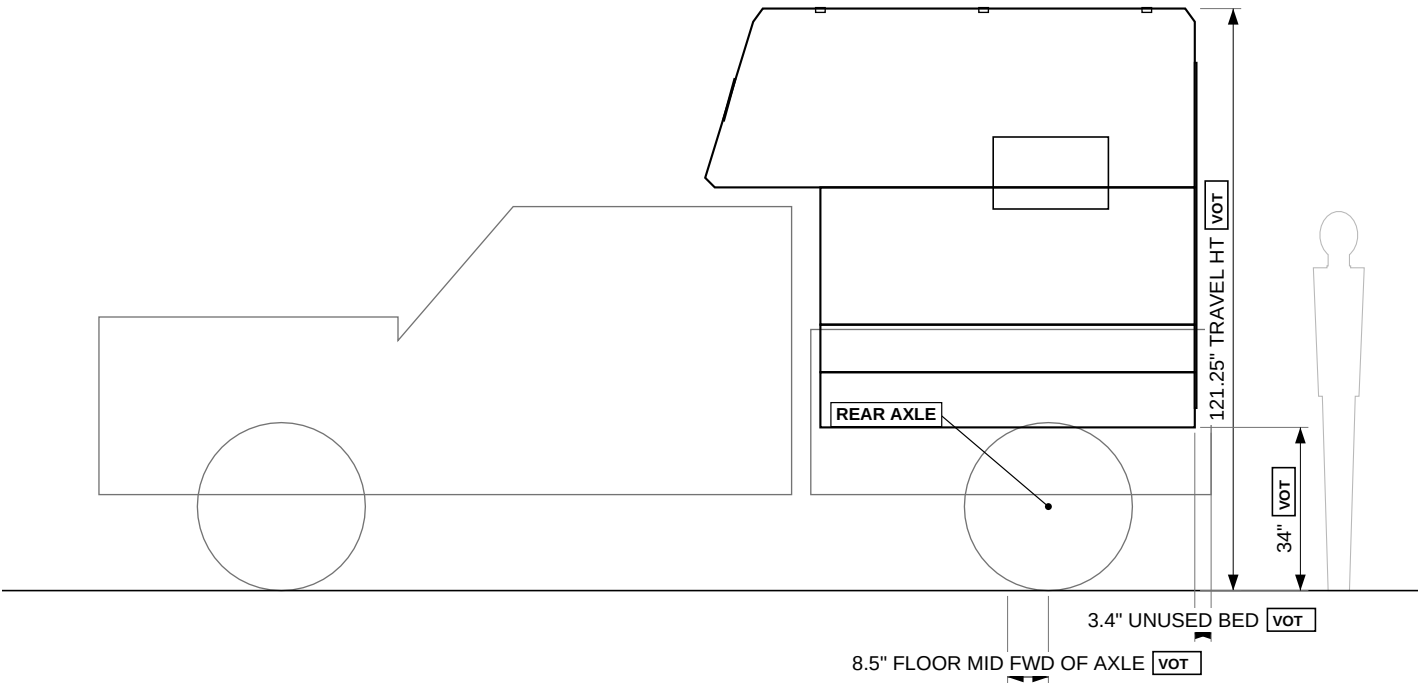

LONG BED (8 FT) - LEFT ELEVATION

SCALE 1:40

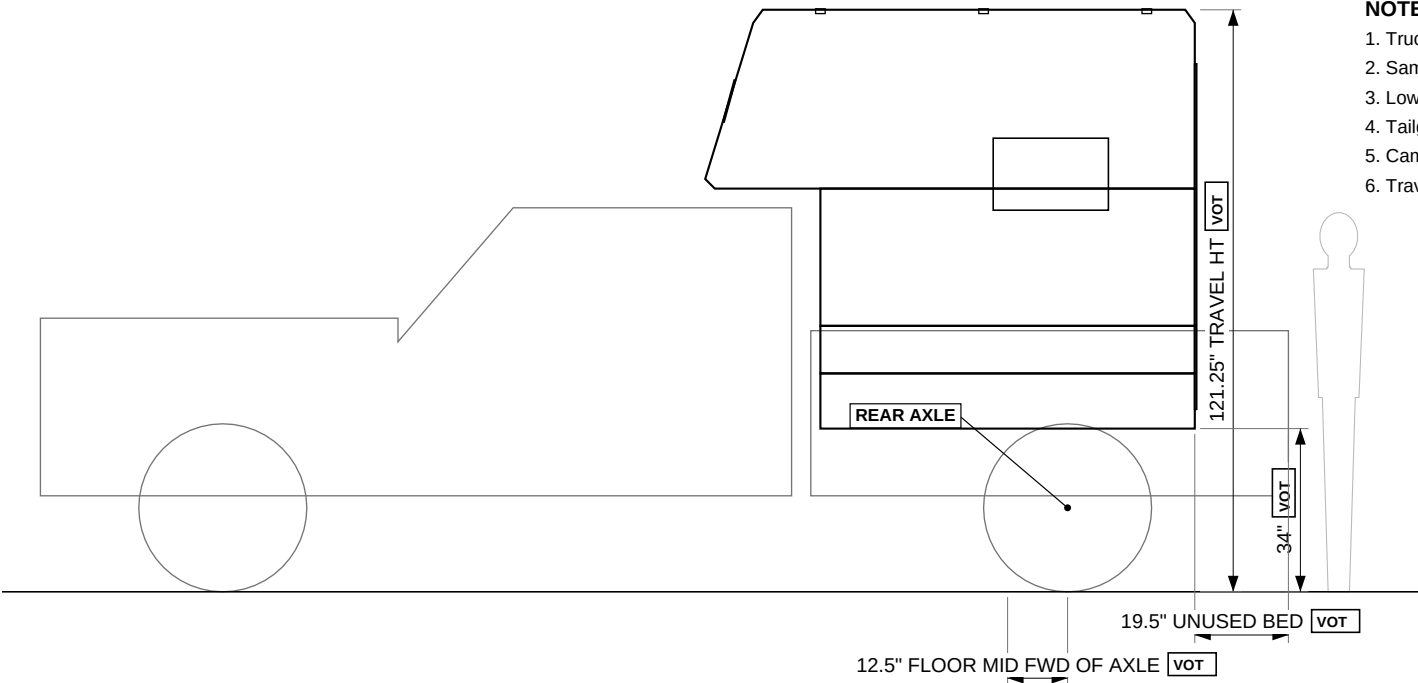

NOTES

1. Truck is a simplified reference; every interface value is VERIFY ON TRUCK (VOT).
2. Same camper fits both beds; on the 8 ft bed the unused length is behind the camper.
3. Lower tub must pass the tailgate opening: tub 63.0" vs opening 65.0" (VOT).
4. Tailgate is not a structural support. Tie-downs and jacks: v0.2.
5. Camper CG must fall forward of the rear axle: v0.2 calculation required.
6. Travel height excludes roof rack and panels.

PROJECT	MINUTEMAN aluminum slide-in camper shell - v0.1 envelope
TITLE	TRUCK FIT - F-350 SHORT AND LONG BED
DWG NO.	A03 REV A DATE 2026-10-01
SCALE	AS NOTED UNITS: INCHES SHEET: ANSI B
STATUS	PRELIMINARY - CONCEPT ENVELOPE - NOT FOR FABRICATION